



VARIANTE A — Pont à tablier mixte (béton armé + poutres acier)

Profil longitudinal | Portée 4 × 15,70 m = 62,80 m

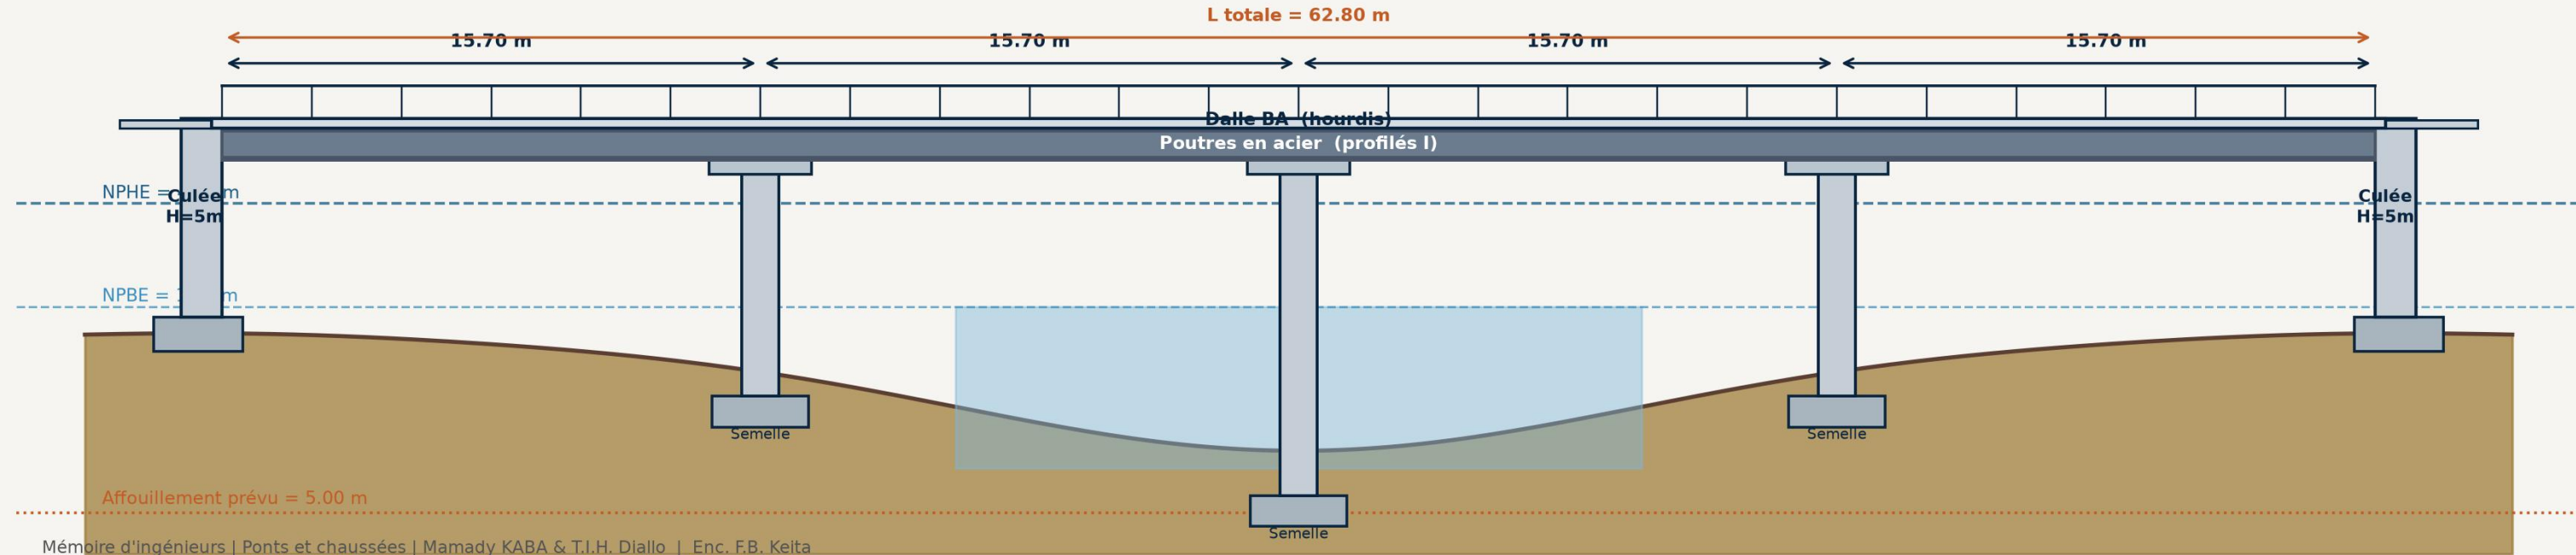


VARIANTE A — Vue en plan | Tablier mixte | Largeur utile 8,00 m

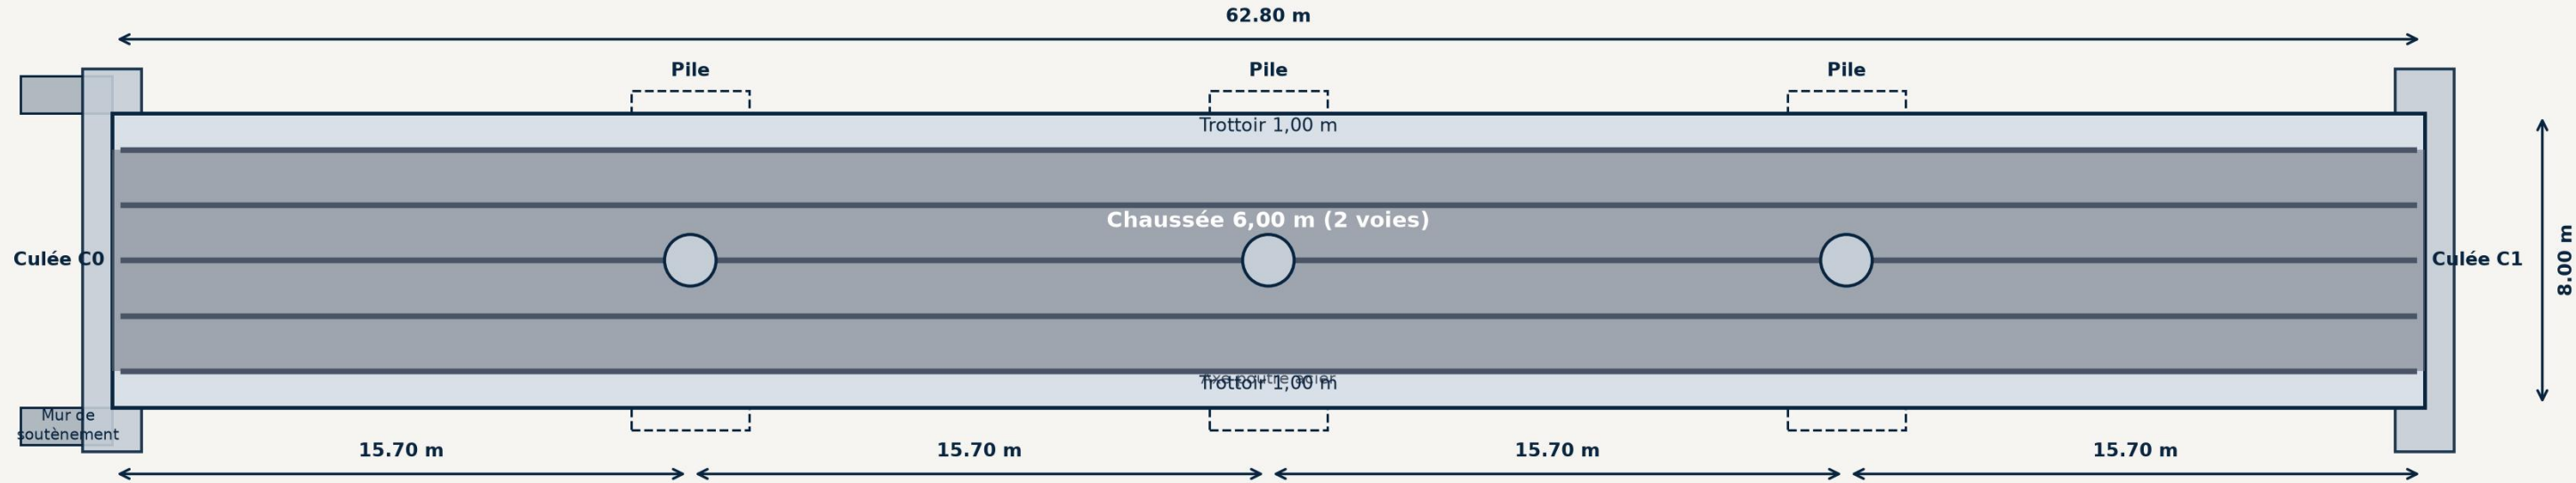

VARIANTE A — Coupe transversale du tablier mixte (dalle en béton armé collaborante + 5 poutres en acier)


Largeur totale = 8.00 m

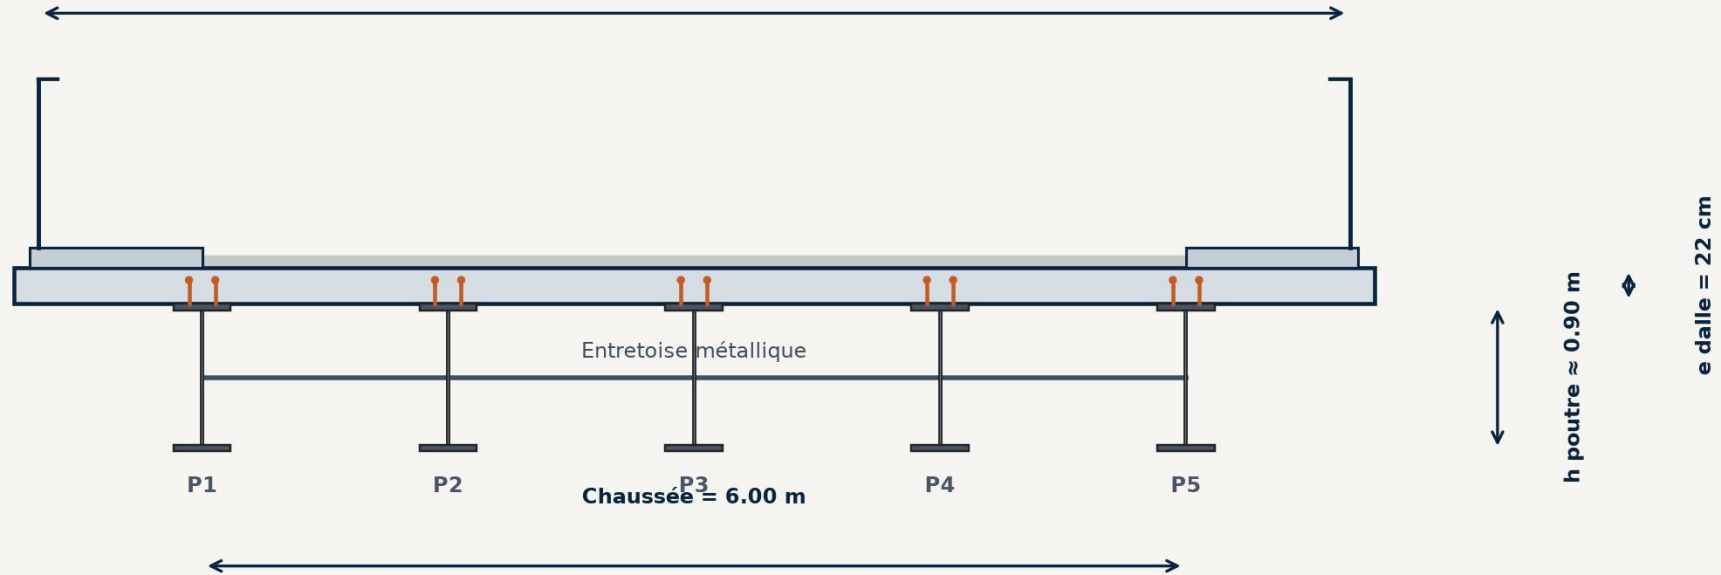


Goujons de connexion • Poutre I acier • Dalle BA collaborante • Action mixte

Avantages : allègement du tablier, grandes portées, montage rapide, faible hauteur constructive


VARIANTE A — Détail de connexion mixte acier/béton et appui sur chevêtre

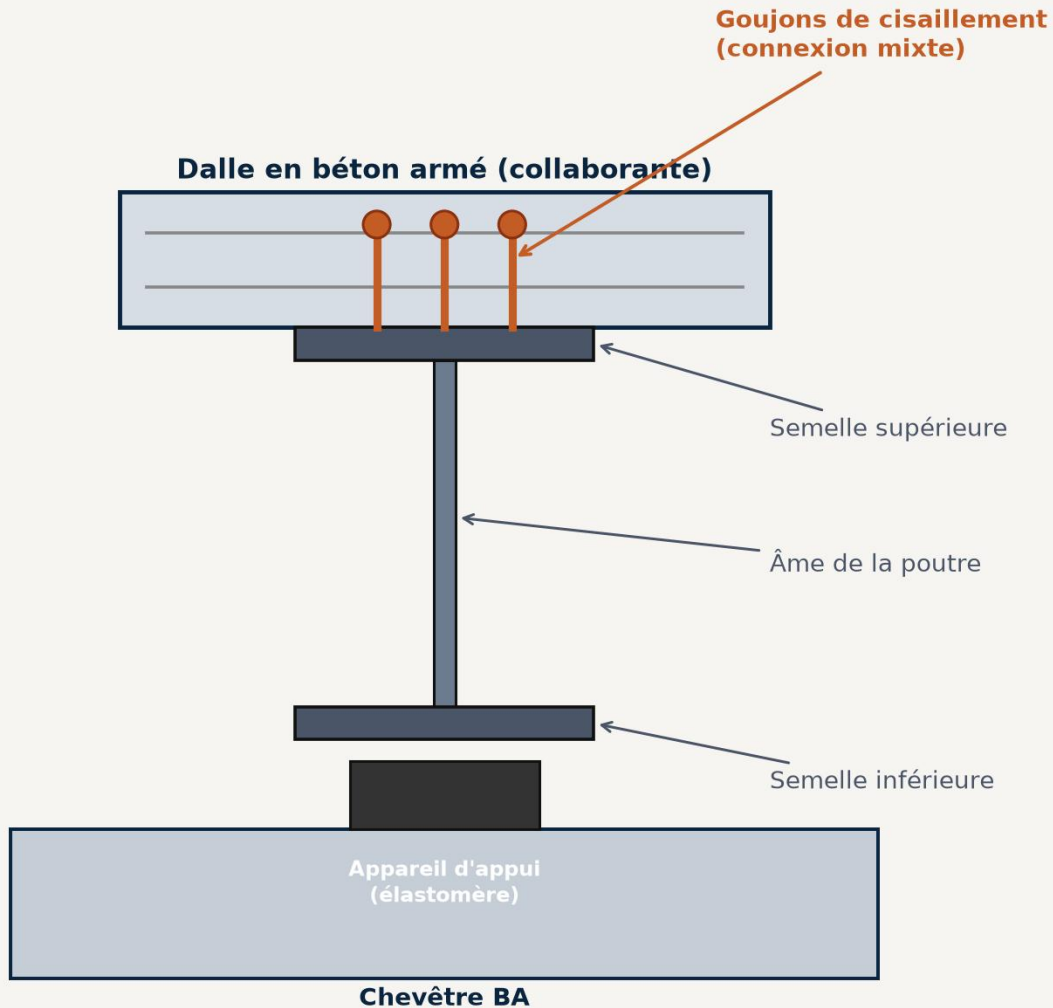

VARIANTE B — Pont en béton précontraint (poutres préfabriquées + hourdis)
Profil longitudinal | Portée 4 × 15,70 m = 62,80 m

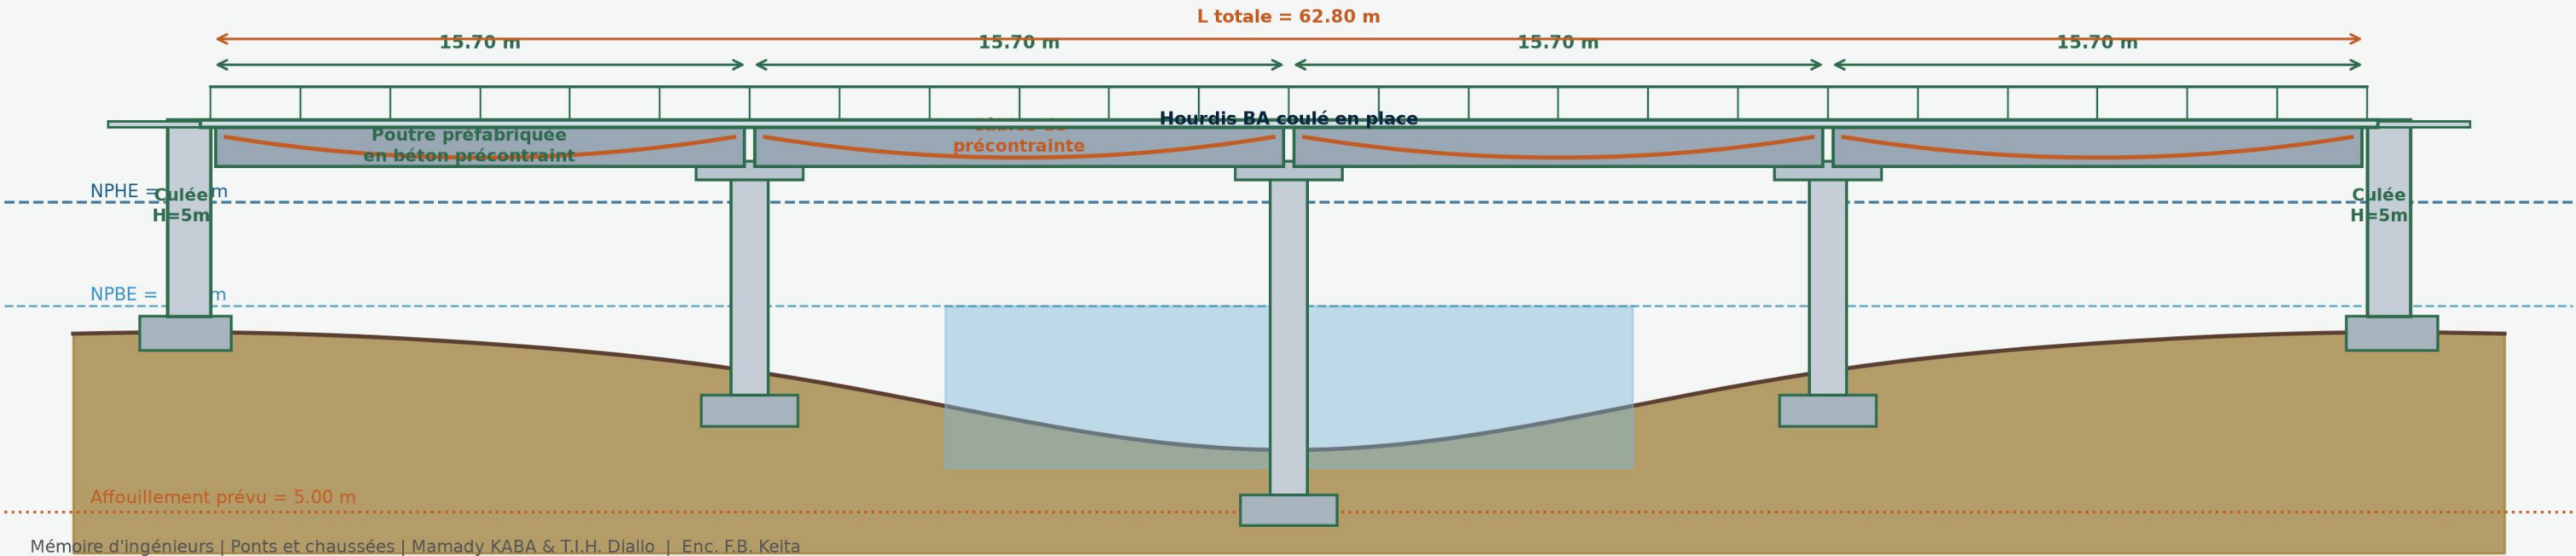


VARIANTE B — Vue en plan | Béton précontraint | Largeur utile 8,00 m

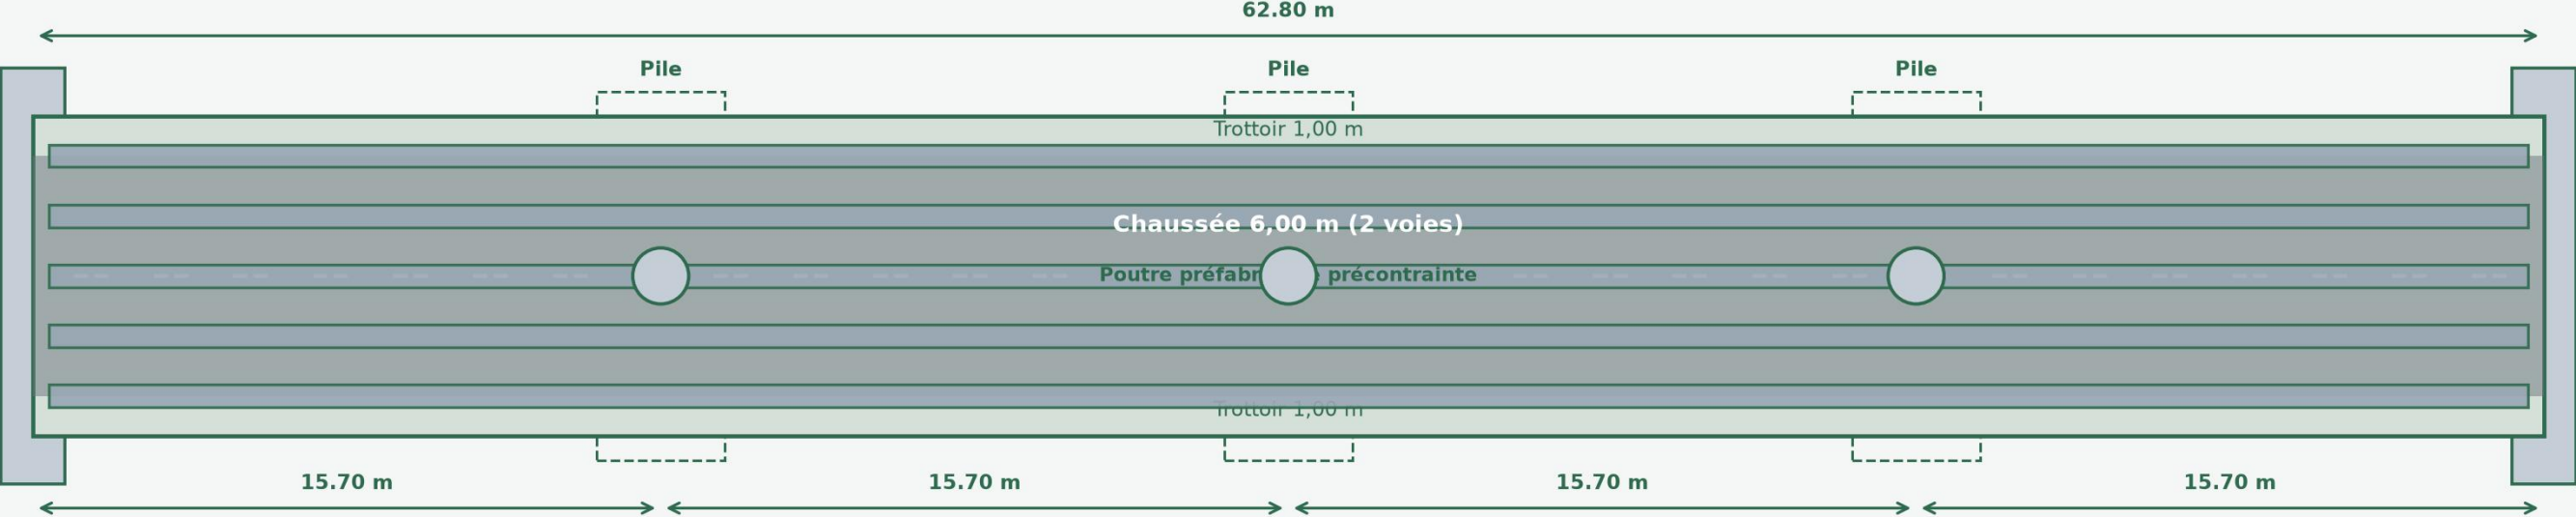

VARIANTE B — Coupe transversale (5 poutres en béton précontraint + hourdis BA)


Largeur totale = 8.00 m

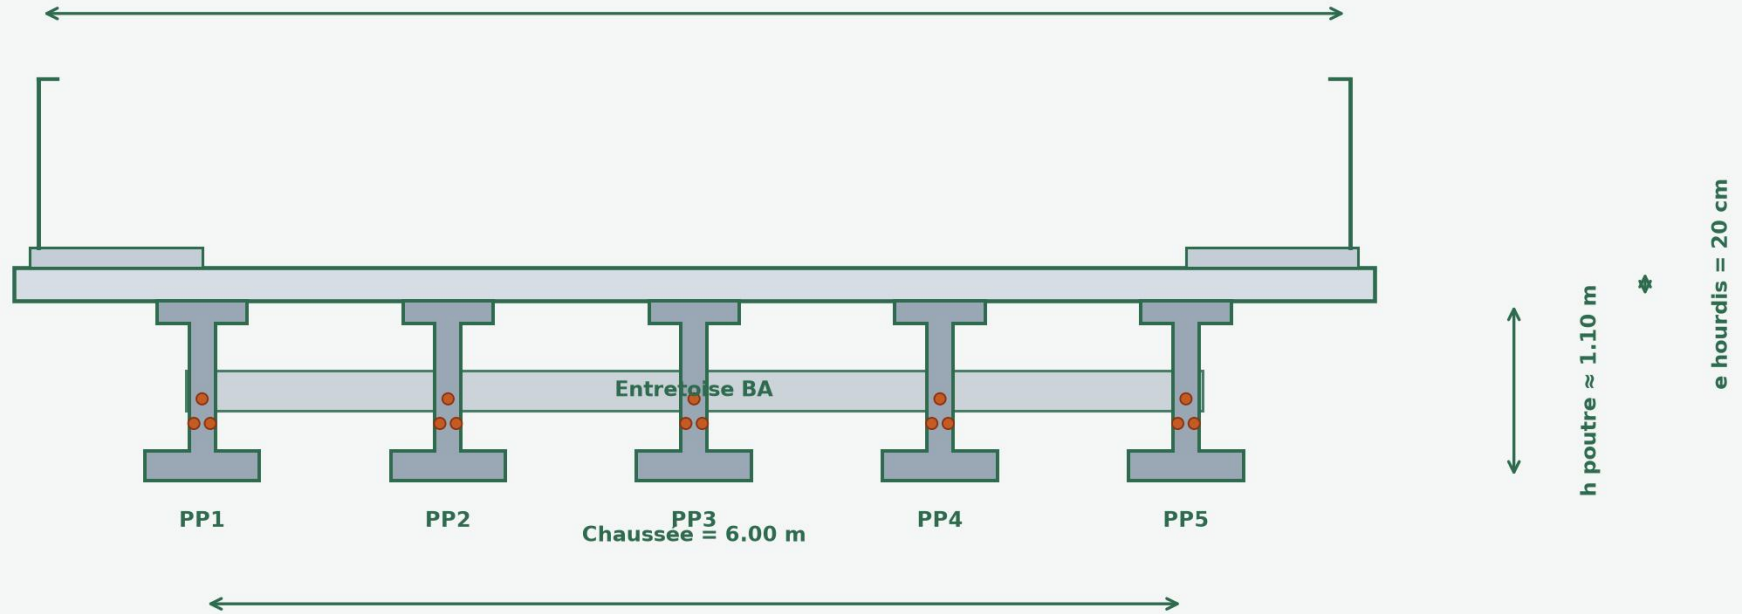

Poutres I préfabriquées précontraintes • Câbles (cercles) • Hourdis collaborant

Avantages : contrôle qualité en usine, montage rapide, excellente durabilité, faible entretien


VARIANTE B — Détail de la poutre précontrainte et appui sur chevêtre

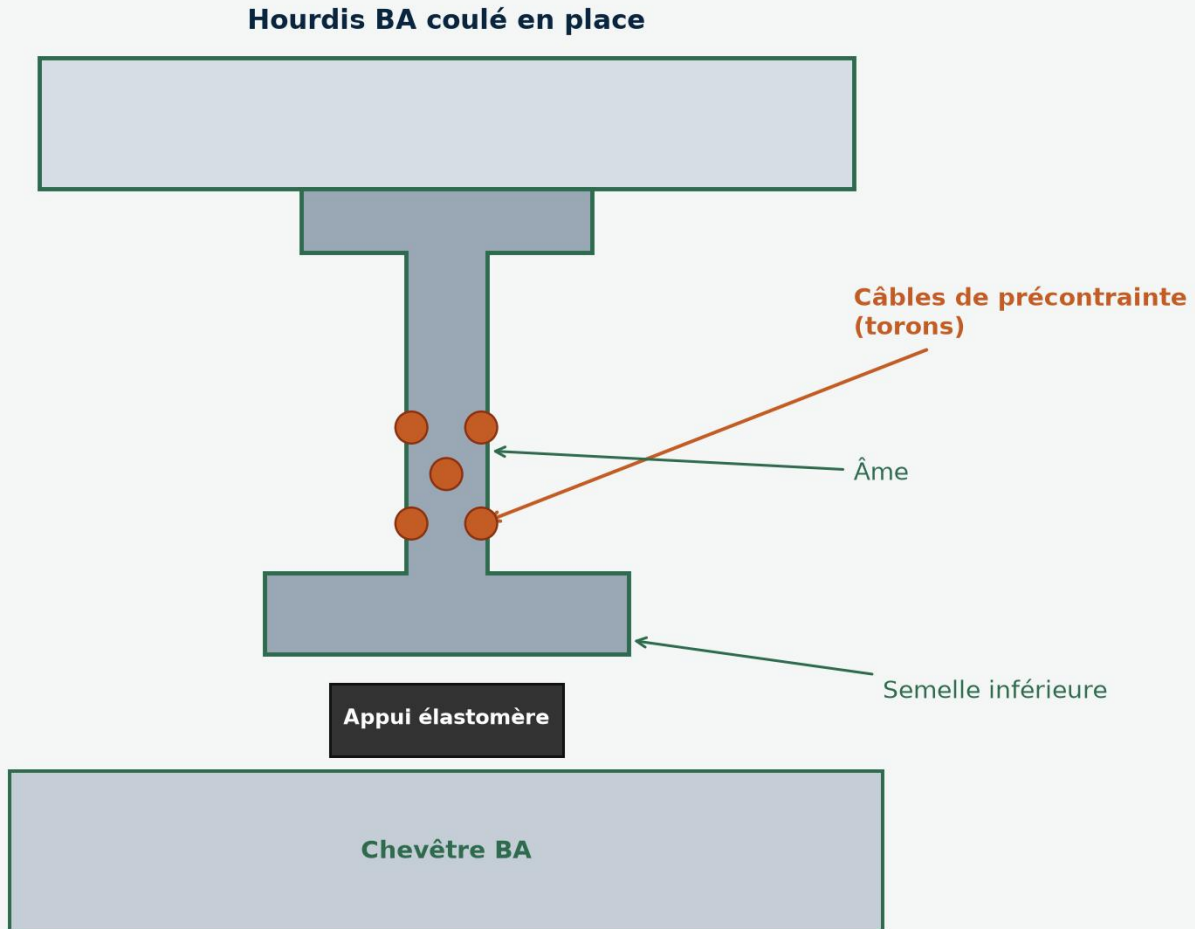

COMPARAISON ARCHITECTURALE DES DEUX VARIANTES


Pont — Portée totale 62.80 m | Largeur 8.00 m

A — Tablier mixte

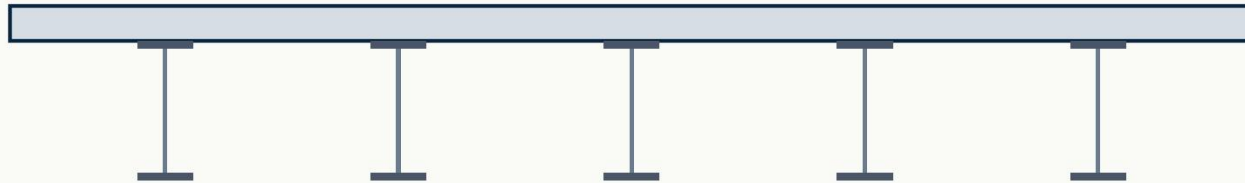




- Dalle BA + poutres acier I
- Connexion par goujons
 - Tablier plus léger
- Montage métallique rapide
- Bon pour portées moyennes
- L = 62.80 m (4×15.70)

B — Béton précontraint

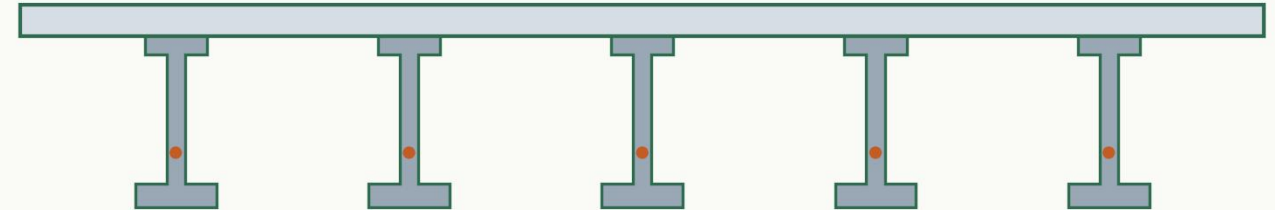

- Poutres I préfabriquées
- Précontrainte par torons
 - Grande durabilité
 - Entretien réduit
- L = 62.80 m (4×15.70)



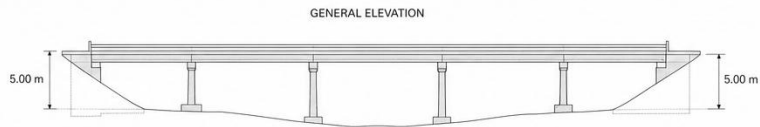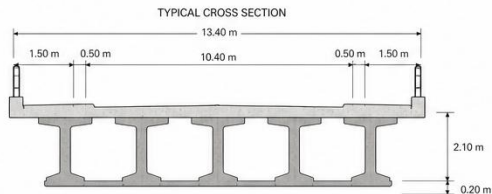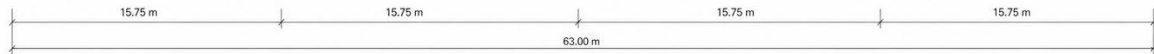

NOTES:

- Structure: Prestressed Concrete Beam Bridge
- Superstructure: Precast Prestressed Concrete I-Girders with Cast-in-Place Concrete Deck
- Spans: 4 @ 15.75 m = 63.00 m
- Substructure: Reinforced Concrete Piers and Abutments
- Deck Width: 13.40 m (Including Sidewalks)
- Design Standard: AASHTO LRFD

KEY SECTION (LONGITUDINAL)

SPAN	SPAN LENGTH	C/C PIER SPACING	TOTAL LENGTH	SKEW	PIER TYPE	FOOTING TYPE
4	15.75 m	15.75 m	63.00 m	0°	Solid Rectangular	Spread Footing